

# TMC FOLDING


1. 판넬의 심재는 내수성이 우수한 18mm 방수PB를 사용한다.
2. 판넬의 마감재는 내수성,내마모성,내화성이 KS기준을 충족하는, HPM으로 한다.
3. 판넬의 마감면은  PVC 에지를 사용한다.
4. 잠금쇠는 사용중임을 표시할 수 있는 유무표시장치와, 외부에서 열수있는 비상키 기능이 있어야 한다.
5. 접이문은 상부 레일·로라로 여닫고, 문짝은 접이문 경첩으로 연결한다.
6. 라미네이트 복합판의 SIZE의 현장 상황에 따라 변할 수 있으므로 현장 실측에 의한 도면작성 후 감독관과 협의후 시공한다.

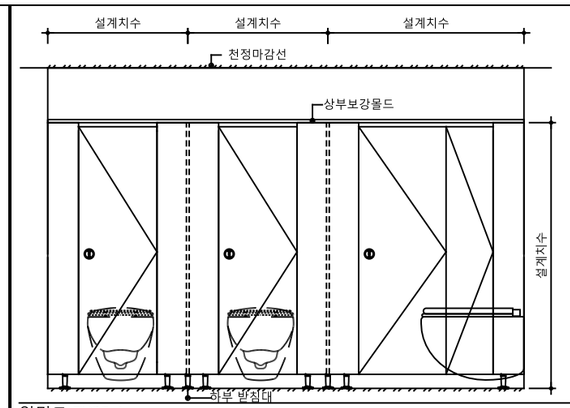



입면도 TYPE A

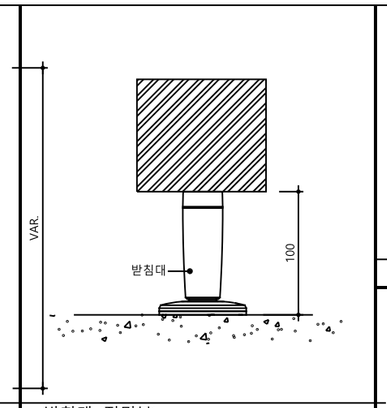



받침대 (전면부)

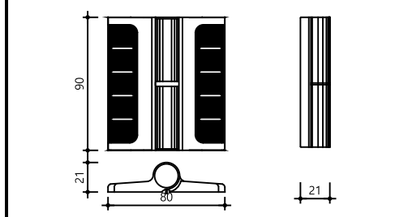



하드웨어 - 접이문 경첩

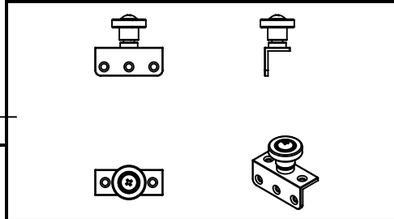


하드웨어 - 로라

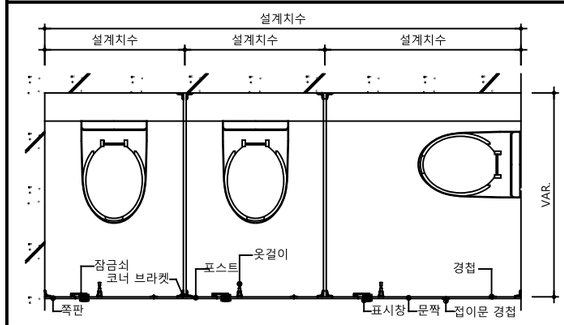


평면도

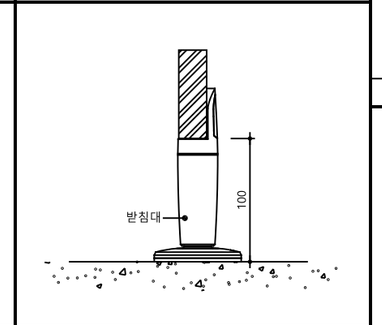



받침대 (측면부)

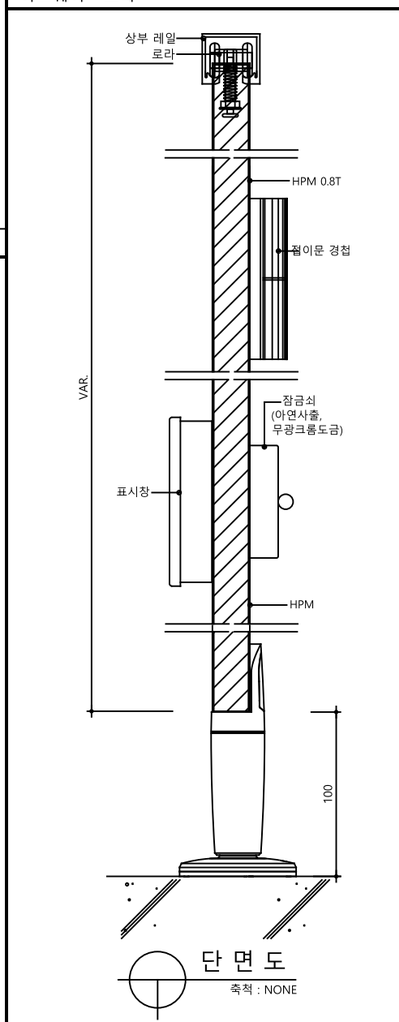


단 면 도

축척 : NONE

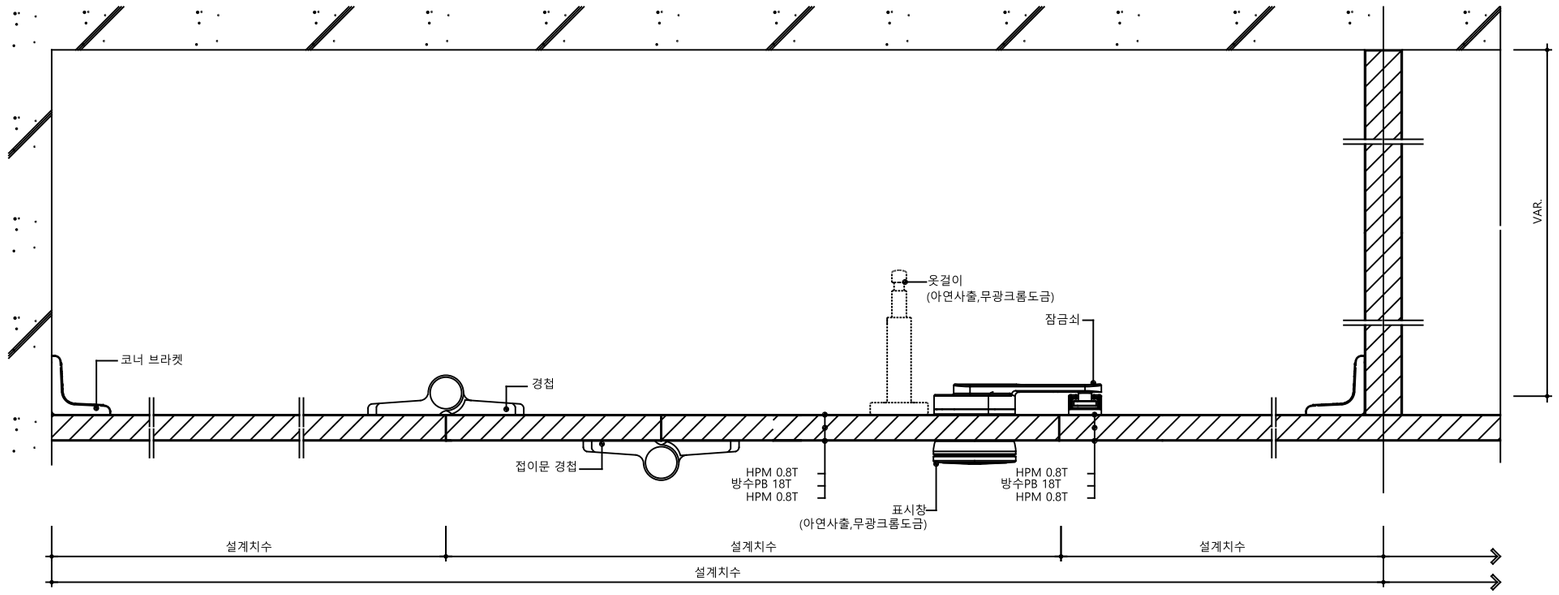


판 넬 상 세 도

축척 : NONE

| |
|---|
| ITEM TITLE |
| TMC FOLDING_01 |
| SCALE |
| NONE |
| DATE |
| |
| DRAWING NO |
| |


TMC
(태민 큐비클)

경기도 남양주시 진접읍 장현리 696-2
T. 031. 571. 3923
F. 031. 571. 3924