

TMC SLIDE


1. 판넬의 심재는 내수성이 우수한 18mm 방수PB를 사용한다.
2. 판넬의 마감재는 내수성,내마모성,내화성이 KS기준을 충족하는, HPM으로 한다.
3. 판넬의 마감면은 PVC 에지를 사용한다.
4. 잠금쇠는 사용중임을 표시할 수 있는 유무표시장치와, 외부에서 열수있는 비상키 기능이 있어야 한다.
5. 미닫이문은 상부 레일·로라로 여닫고, 하부 가이드로 흔들림을 잡는다.
6. 라미네이트 복합판의 SIZE의 현장 상황에 따라 변할 수 있으므로 현장 실측에 의한 도면작성 후 감독관과 협의후 시공한다.

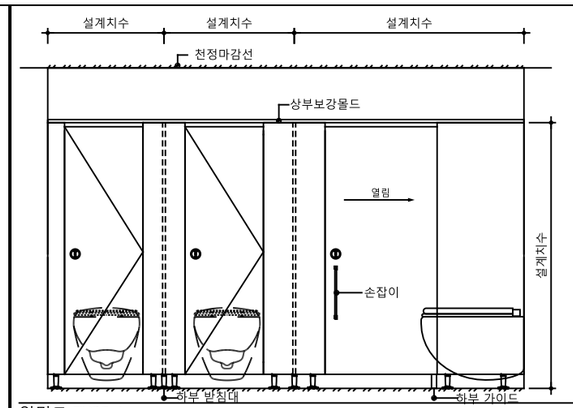


입면도 TYPE A

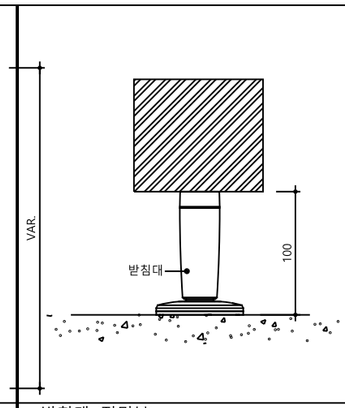


받침대 (전면부)

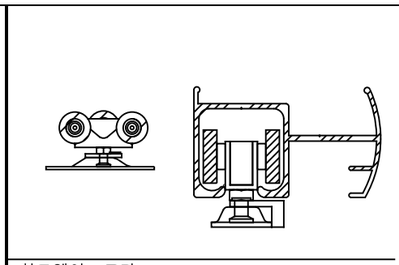


하드웨어 - 로라

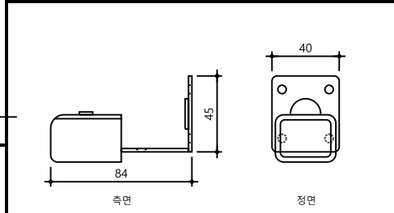


하드웨어 - 하부 가이드

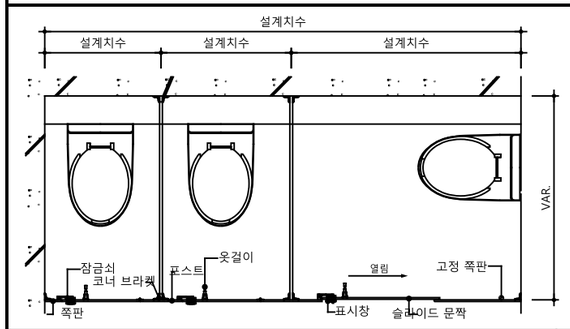

평면도

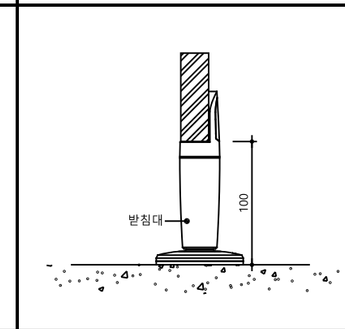


받침대 (측면부)

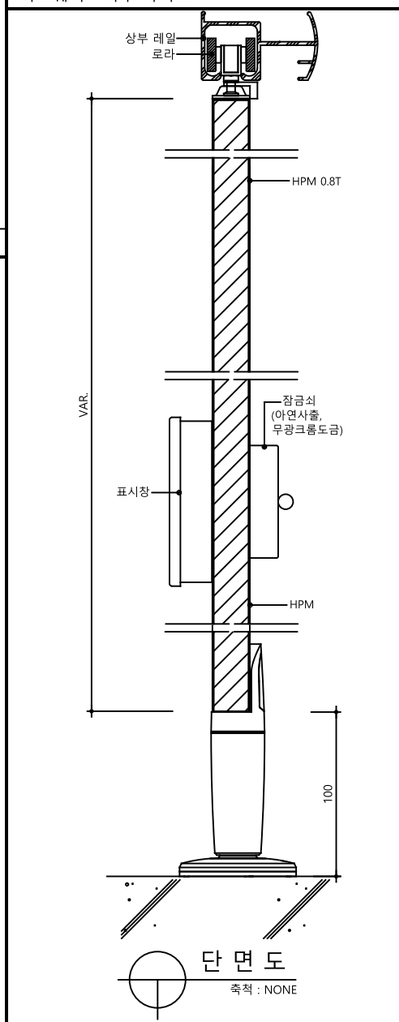

단 면 도

축척 : NONE

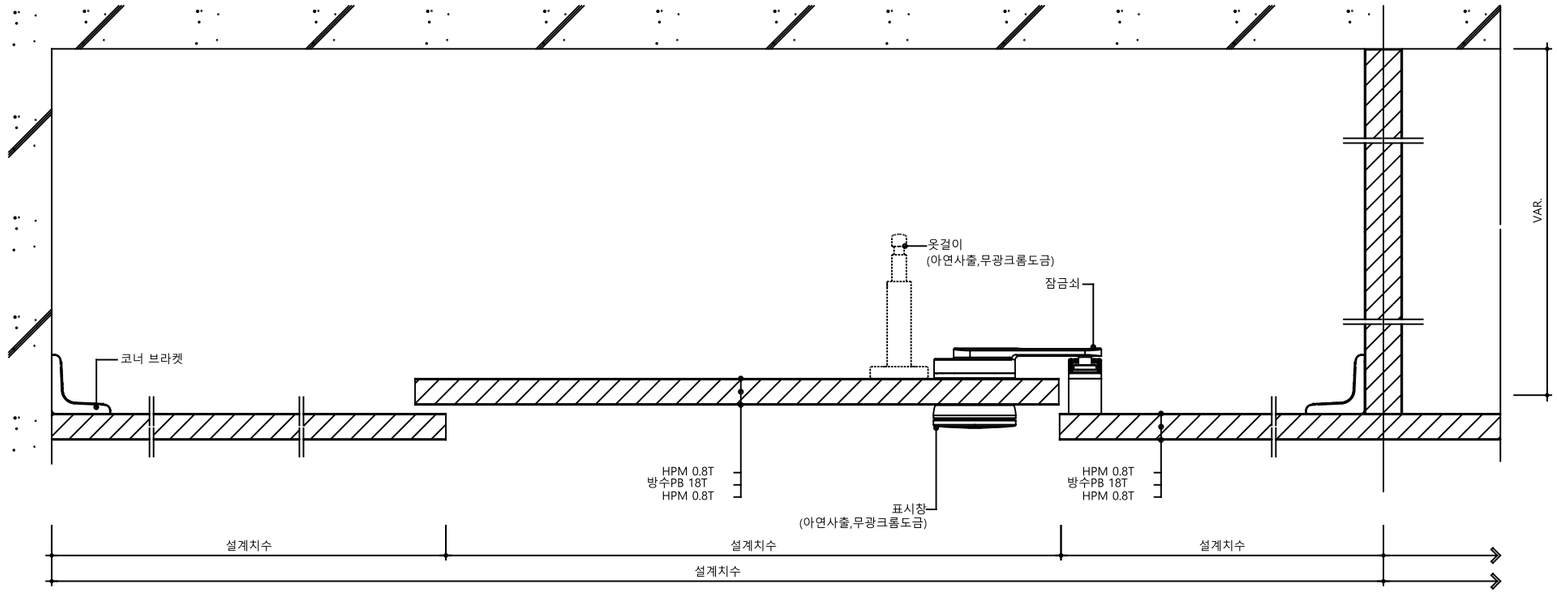

판 넬 상 세 도

축척 : NONE

ITEM TITLE
TMC SLIDE_01
SCALE
NONE
DATE
DRAWING NO

TMC
(태민 큐비클)

경기도 남양주시 진접읍 장현리 696-2
T. 031. 571. 3923
F. 031. 571. 3924