TMC UNI

1. 판넬의 심재는 내수성이 우수한 18mm 방수PB를 사용한다.

2. 판넬의 마감재는 내수성,내마모성,내화성이 KS기준을 충족하는,
   HPM으로 한다. 도어 전면부는 주문형 디자인 HPM을 사용한다.


3. 판넬의 마감면은 PVC 에지를 사용한다.

4. 잠금쇠는 사용중임을 표시할 수 있는 유무표시장치와,
   외부에서 열수있는 비상키 기능이 있어야 한다.


5. 도어 경첩은 상시열림각을 15~30도로 조정할 수 있어야 한다.

6. 포스트 및 측면칸막이 벽체 하단에는 별도의 스텐리스 재질의 안심스크린을
   설치한다.


7. 라미네이트 복합판의 SIZE의 현장 상황에 따라 변할 수 있으므로
   현장 실측에 의한 도면작성 후 감독관과 협의후 시공한다.

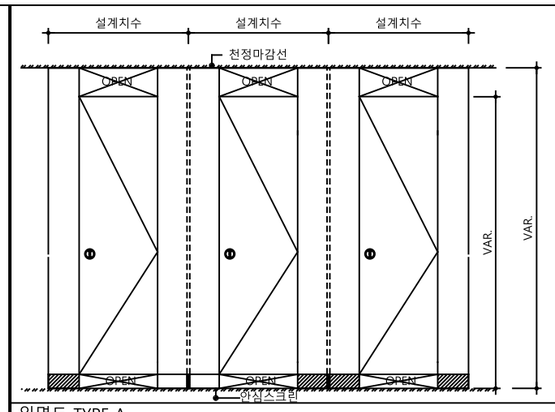


입면도 TYPE A

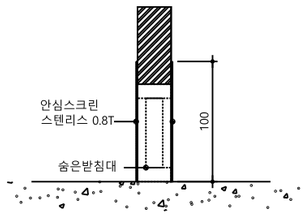


안심스크린 상세(전면부)

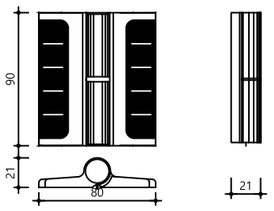


하드웨어 - 경첩

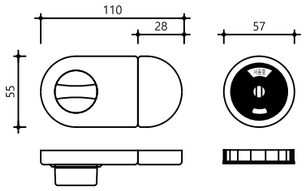


하드웨어 - 잠금쇠

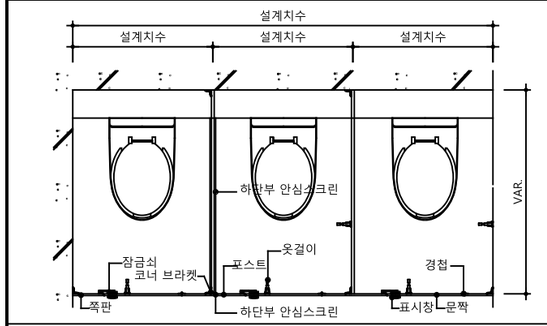

평면도

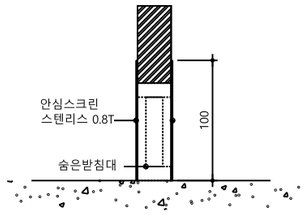


안심스크린(측면부)

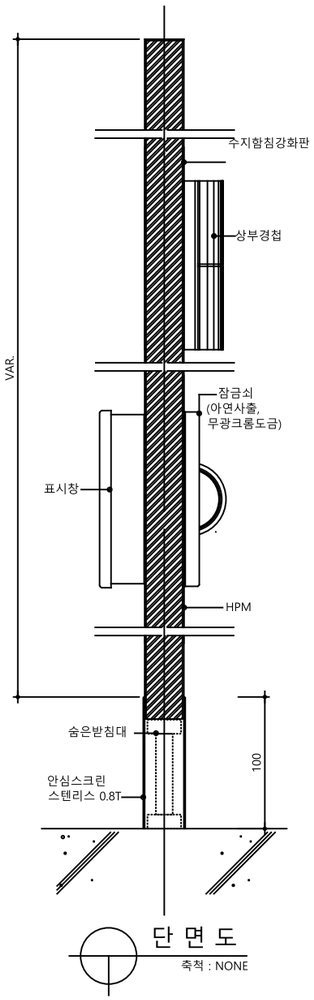

단 면 도

축척 : NONE

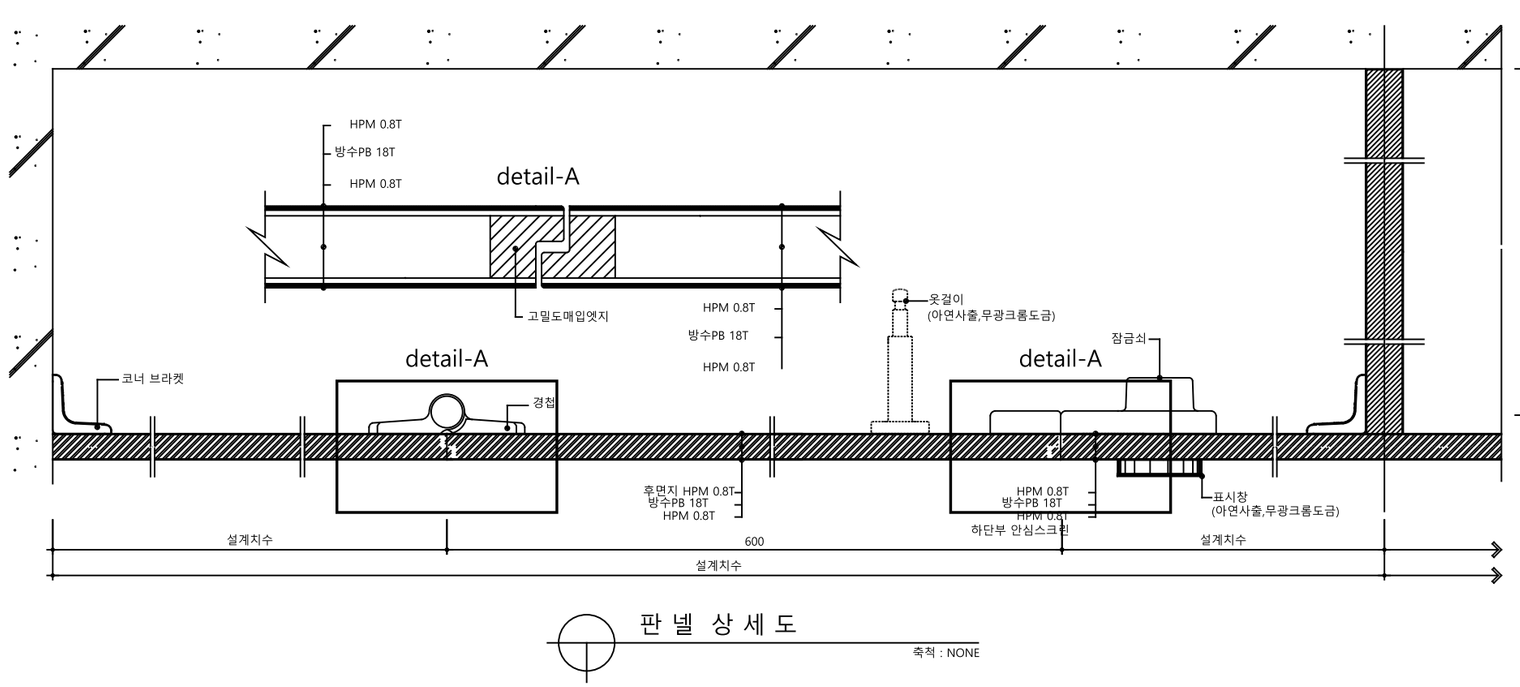

판 넬 상 세 도

축척 : NONE

ITEM TITLE
TMC-UNI-07
SCALE
NONE
DATE
DRAWING NO

TMC
(태민 큐비클)

경기도 남양주시 진접읍 장현리 696-2
T. 031. 571. 3923
F. 031. 571. 3924