



TMC EDGE


1. 판넬의 심재는 내수성이 우수한 18mm 방수PB를 사용한다.
2. 판넬의 마감재는 내수성,내마모성,내화성이 KS기준을 충족하는, HPM으로 한다,
3. 판넬의 마감면은 PVC 에지를 사용한다.
4. 잠금쇠는 사용중임을 표시할 수 있는 유무표시장치와, 외부에서 열수있는 비상키 기능이 있어야 한다,
5. 도어 경첩은 상시열림각을 15~30도로 조정할 수 있어야 한다,
6. 포스트 및 측면칸막이 벽체 하단에는 별도의 스텐리스 재질의 안심스크린을 설치한다,
7. 라미네이트 복합판의 SIZE의 현장 상황에 따라 변할 수 있으므로 현장 실측에 의한 도면작성 후 감독관과 협의후 시공한다,

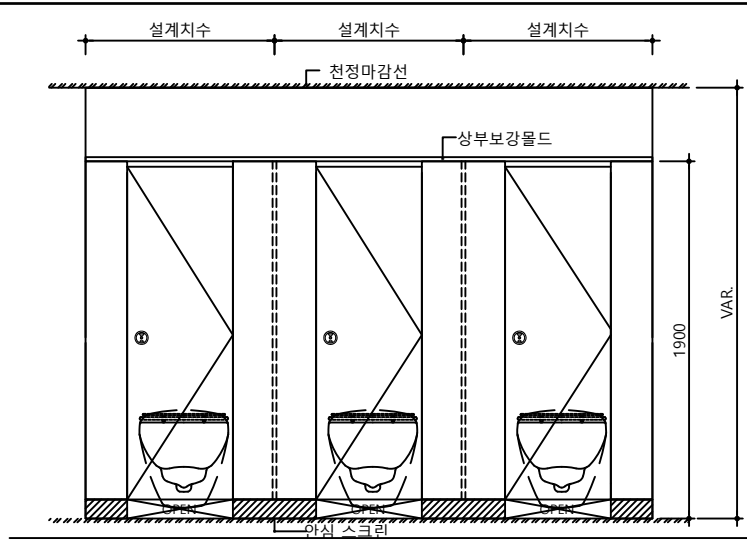


입면도 TYPE A

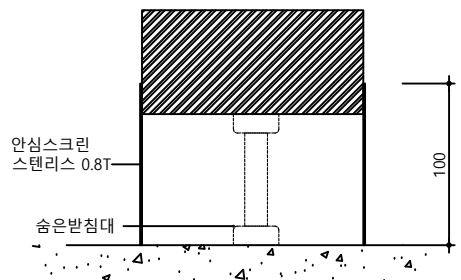


안심스크린 상세(전면부)

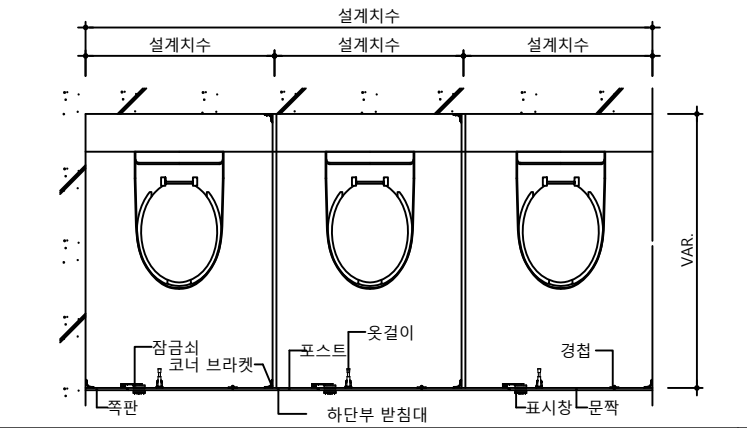


평면도

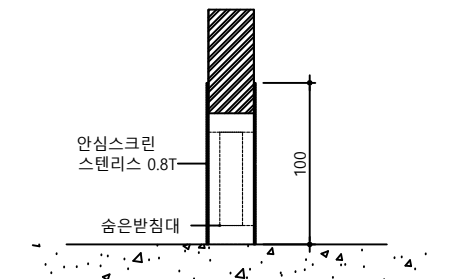



안심스크린(측면부)

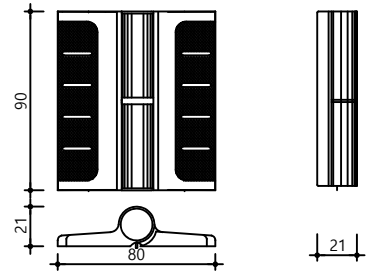

하드웨어 - 경첩

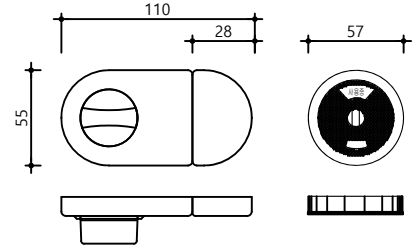

하드웨어 - 잠금쇠

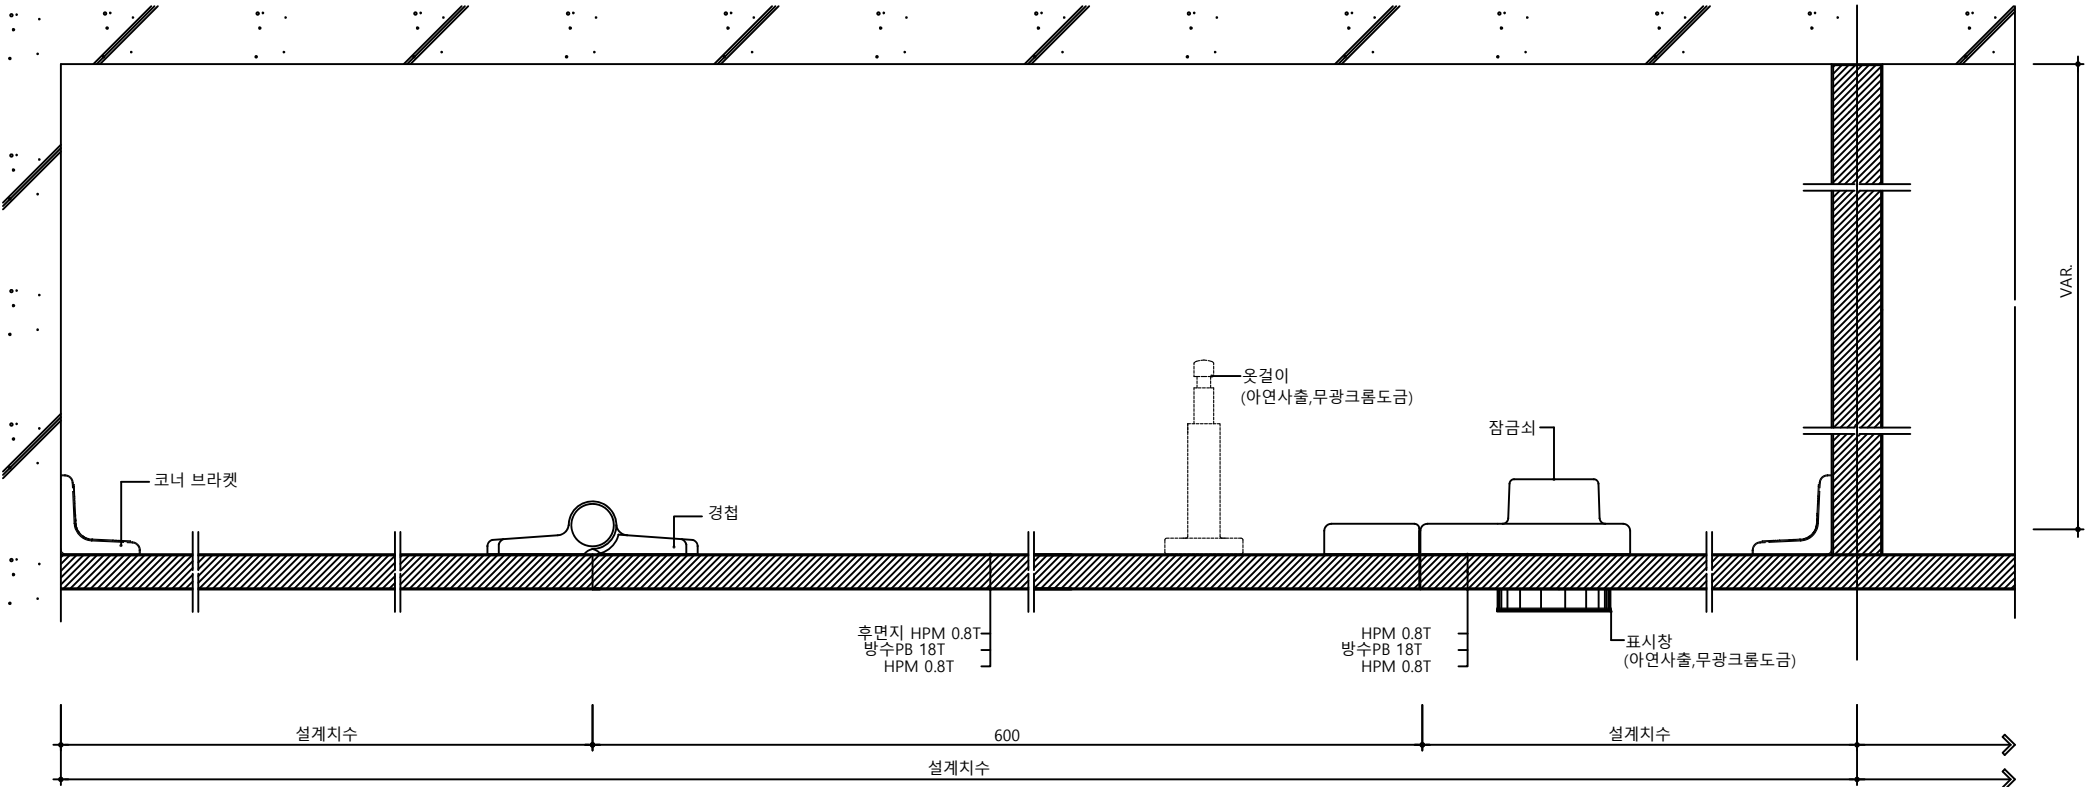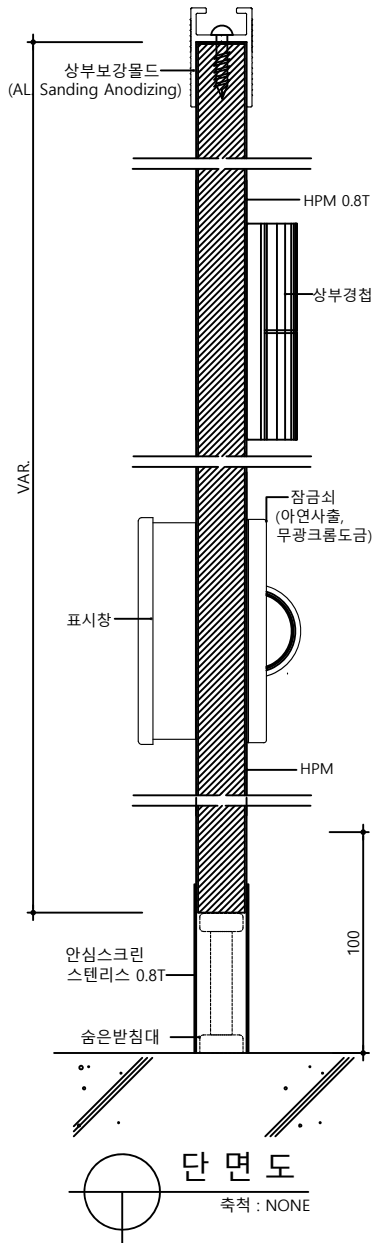

판넬 상세도

축척 : NONE

ITEM TITLE

TMC EDGE_37

SCALE

NONE

DATE

DRAWING NO

TMC
(태민 큐비클)

경기도 남양주시 진접읍 장현리 696-2
T. 031. 571. 3923
F. 031. 571. 3924