



TMC 스테인리스 스틸(STS304)


1. 판넬의 심재는 코아합판 사용한다.
2. 포스트 판의 마감재는 내수성,내마모성,내화성이 KS 기준을 충족하는,
STS 304로 한다.
4. 잠금쇠는 사용중임을 표시할 수 있는 유무표시장치와,
외부에서 열수있는 비상키 기능이 있어야 한다.
5. 도어 경첩은 상시열림각을 15~30도로 조정할 수 있어야 한다.
6. 포스트 및 측면칸막이 벽체 하단에는 별도의 스테인리스 재질의 안심스크린을
설치한다.
7. STS 304 SIZE는 현장 상황에 따라 변할 수 있으므로
현장 실측에 의한 도면작성 후 감독관과 협의후 시공한다.

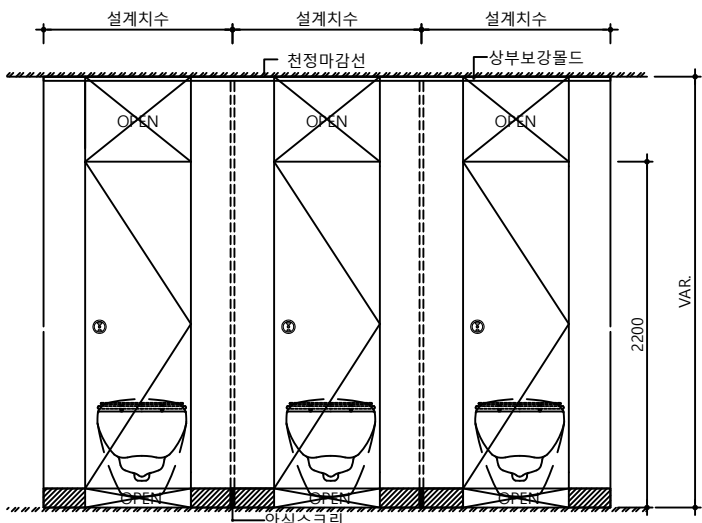


입면도 TYPE A

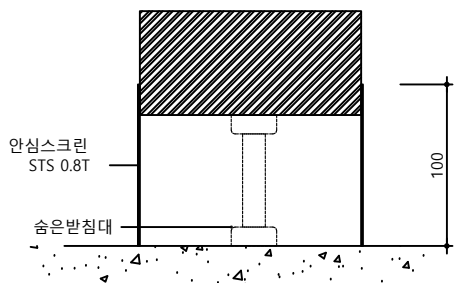


안심스크린 상세(전면부)

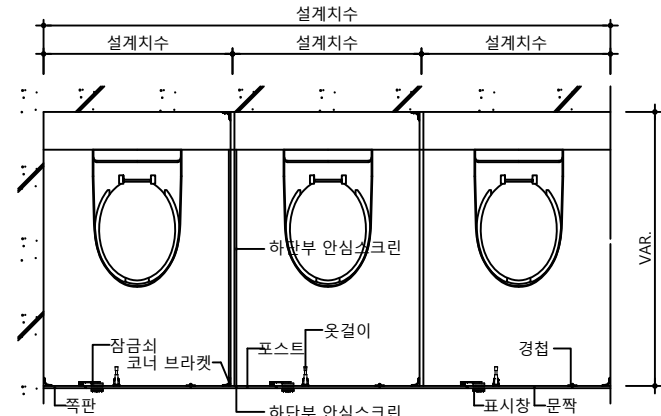


평면도

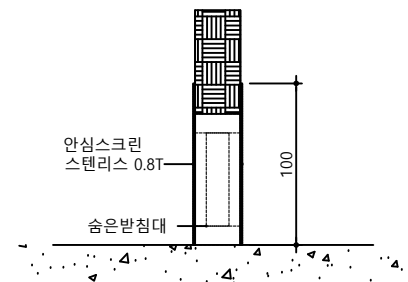


안심스크린(측면부)

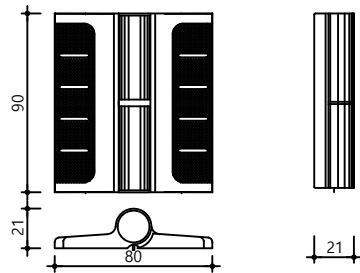


하드웨어 - 경첩

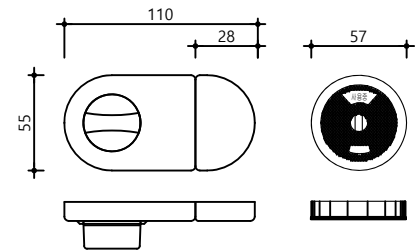

하드웨어 - 잠금쇠

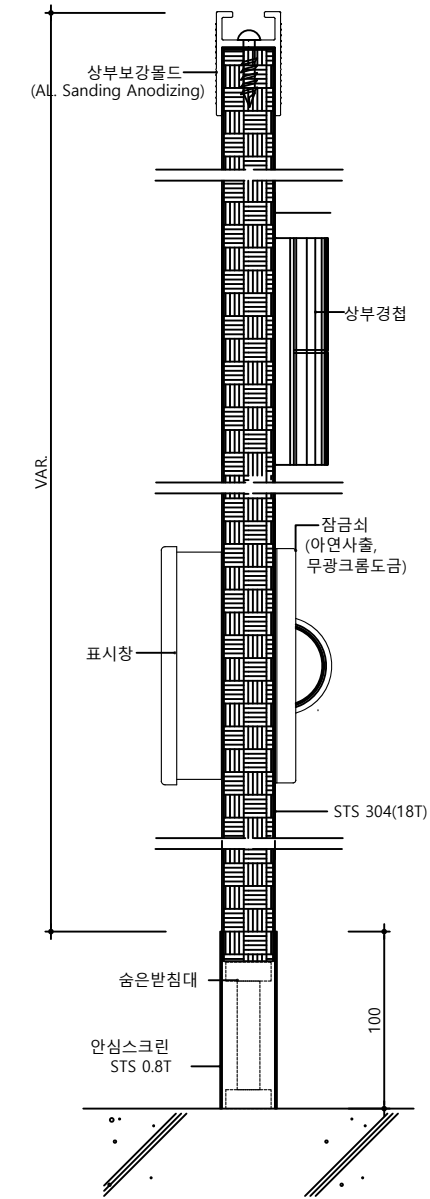

단면도
축척 : NONE

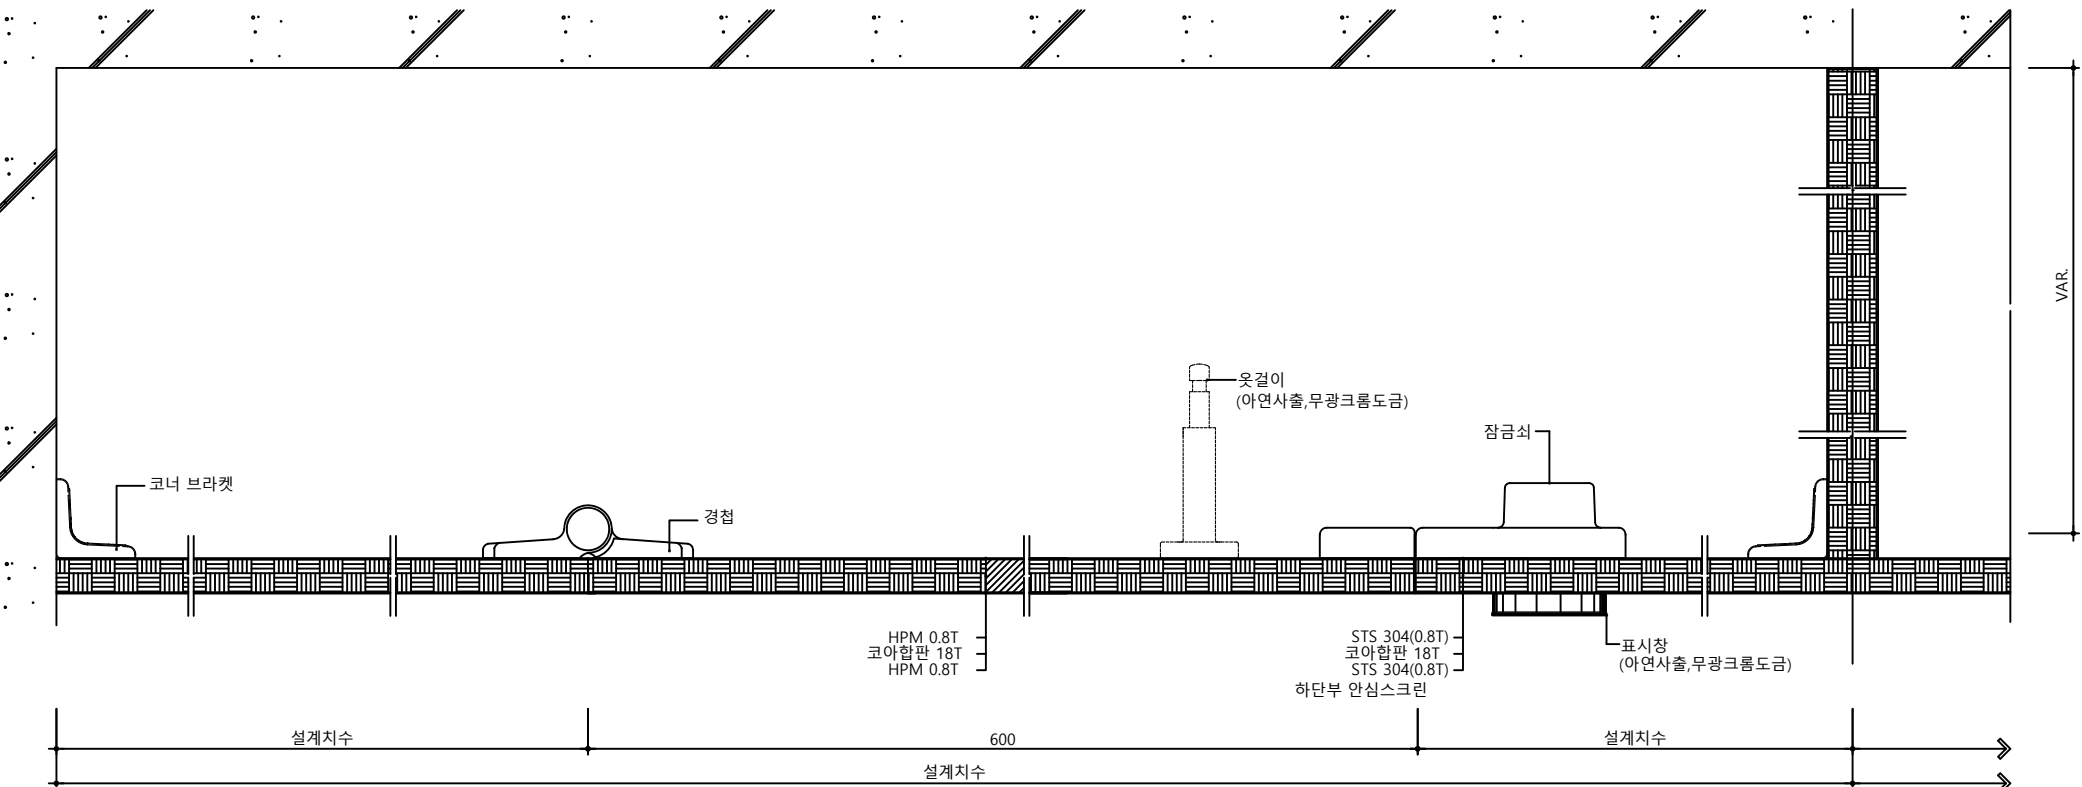

판넬 상세도
축척 : NONE

ITEM TITLE

TMC STS_10

SCALE

NONE

DATE

DRAWING NO

TMC
(태민 큐비클)

경기도 남양주시 진접읍 장현리 696-2
T. 031. 571. 3923
F. 031. 571. 3924